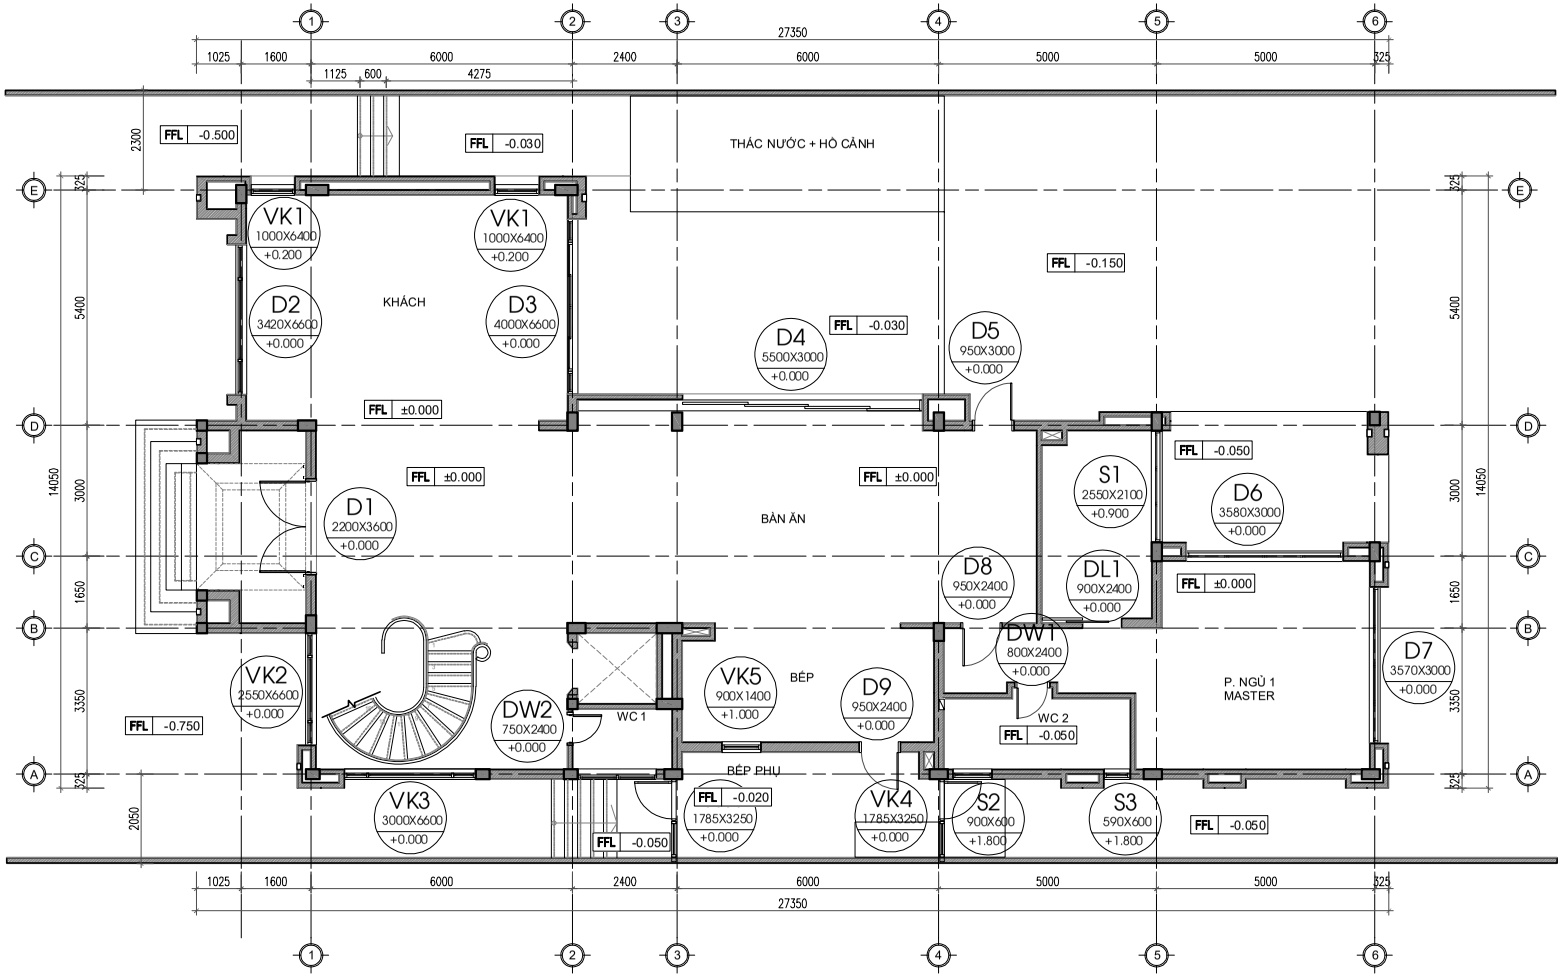


MẶT BẰNG ĐỊNH VỊ CỬA TẦNG 1

LẦN	NGÀY	NỘI DUNG SỬA ĐỔI

CHỦ ĐẦU TƯ - PROJECT OWNER:

ANH ĐỨC ANH

TÊN CÔNG TRÌNH - PROJECT:

BIỆT THỰ VƯỜN

HẠNG MỤC:

KIẾN TRÚC

VỊ TRÍ - LOCATION:

TỈNH HẢI PHÒNG

S - HOUSE DESIGN
INTERIOR DESIGN - CONSTRUCTION

CÔNG TY CỔ PHẦN
S-HOUSE VIỆT NAM
ĐỊA CHỈ: D49 LK7 Ô SỐ 1, KHU ĐÔ THỊ MỚI HAI BÊN ĐƯỜNG LÊ TRỌNG TẤN, PHƯỜNG DƯƠNG NỘI, THÀNH PHỐ HÀ NỘI.
TEL: 0966.005.060
WWW.NHADEPSHOUSE.COM

GIÁM ĐỐC:
DIRECTOR:

GĐ. NGUYỄN VĂN SANG

CHỦ TRÌ KIẾN TRÚC :
PRIMARY ARCHITECT:

KTS.TRƯƠNG QUANG NHẬT

CHỦ TRÌ KẾT CẤU
STRUCTURAL DESIGNER:

KS. ĐỖ MINH KHUÊ

THIẾT KẾ
DESIGNED BY:

KTS. NGUYỄN QUỐC BẢO


TÊN BẢN VẼ:
DRAWING NAME:

MẶT BẰNG ĐỊNH VỊ CỬA TẦNG 1

TỶ LỆ - SCALE:	BẢN VẼ SỐ:
1/70	KT- 45
TÊN FILE - PATH FILE:	

GHI CHÚ/NOTE:

- Kích thước trên bản vẽ phải được kiểm tra thực tế tại công trình, nếu có sai lệch kích thước tại hiện trường phải báo thiết kế kịp thời để trao đổi phương án xử lý. Người thiết kế sẽ không chịu trách nhiệm kích thước tại công trình.
- Bản vẽ & thiết kế thuộc quyền sở hữu của Công ty CP S-House, không được sao chép nếu không có sự chấp thuận từ S-House.
- Hướng cửa xem trên mặt bằng định vị cửa

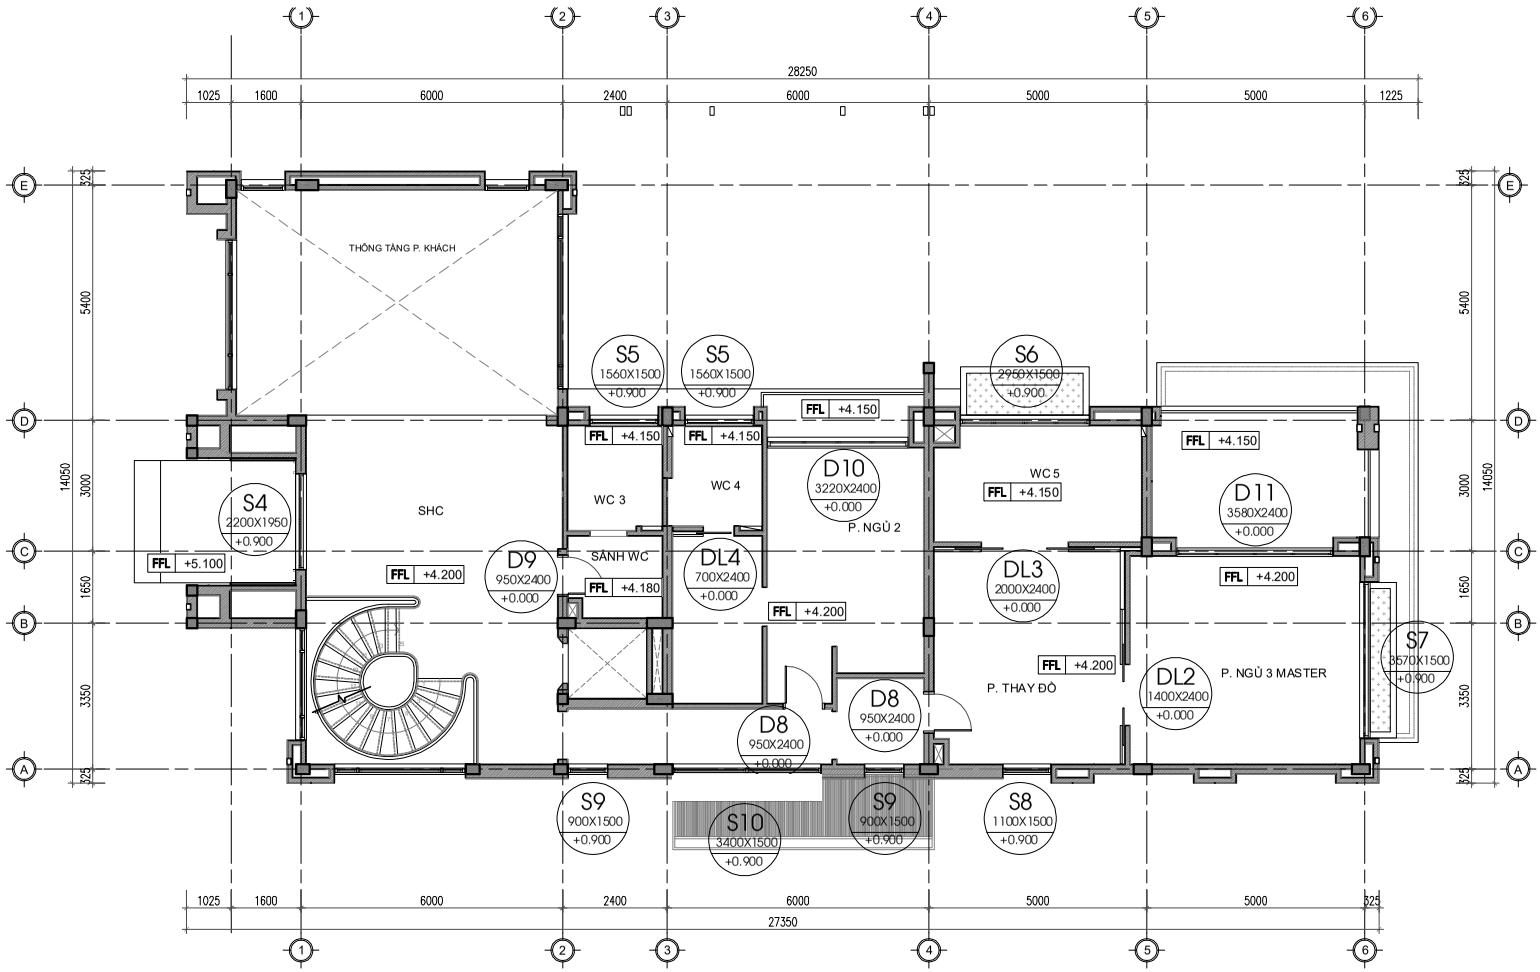

MẶT BẰNG ĐỊNH VỊ CỬA TẦNG 2

LẦN	NGÀY	NỘI DUNG SỬA ĐỔI

CHỦ ĐẦU TƯ - PROJECT OWNER:

ANH ĐỨC ANH

TÊN CÔNG TRÌNH - PROJECT:

BIỆT THỰ VƯỜN

HẠNG MỤC:

KIẾN TRÚC

VỊ TRÍ - LOCATION:

TỈNH HẢI PHÒNG

S - HOUSE DESIGN
INTERIOR DESIGN - CONSTRUCTION

CÔNG TY CỔ PHẦN
S-HOUSE VIỆT NAM
ĐỊA CHỈ: D49 LK7 Ô SỐ 1, KHU ĐÔ THỊ MỚI HAI BÊN ĐƯỜNG LÊ TRỌNG TẤN, PHƯỜNG DƯƠNG NỘI, THÀNH PHỐ HÀ NỘI.
TEL: 0966.005.060
WWW.NHADEPSHOUSE.COM

GIÁM ĐỐC:
DIRECTOR:

GĐ. NGUYỄN VĂN SANG

CHỦ TRÌ KIẾN TRÚC :
PRIMARY ARCHITECT:

KTS.TRƯƠNG QUANG NHẬT

CHỦ TRÌ KẾT CẤU
STRUCTURAL DESIGNER:

KS. ĐỖ MINH KHUÊ

THIẾT KẾ
DESIGNED BY:

KTS. NGUYỄN QUỐC BẢO


TÊN BẢN VẼ:
DRAWING NAME:

MẶT BẰNG ĐỊNH VỊ CỬA TẦNG 2

TỶ LỆ - SCALE:	BẢN VẼ SỐ:
1/70	KT- 46
TÊN FILE - PATH FILE:	

GHI CHÚ/NOTE:

- Kích thước trên bản vẽ phải được kiểm tra thực tế tại công trình, nếu có sai lệch kích thước tại hiện trường phải báo thiết kế kịp thời để trao đổi phương án xử lý. Người thiết kế sẽ không chịu trách nhiệm kích thước tại công trình.
- Bản vẽ & thiết kế thuộc quyền sở hữu của Công ty CP S-House, không được sao chép nếu không có sự chấp thuận từ S-House.
- Hướng cửa xem trên mặt bằng định vị cửa

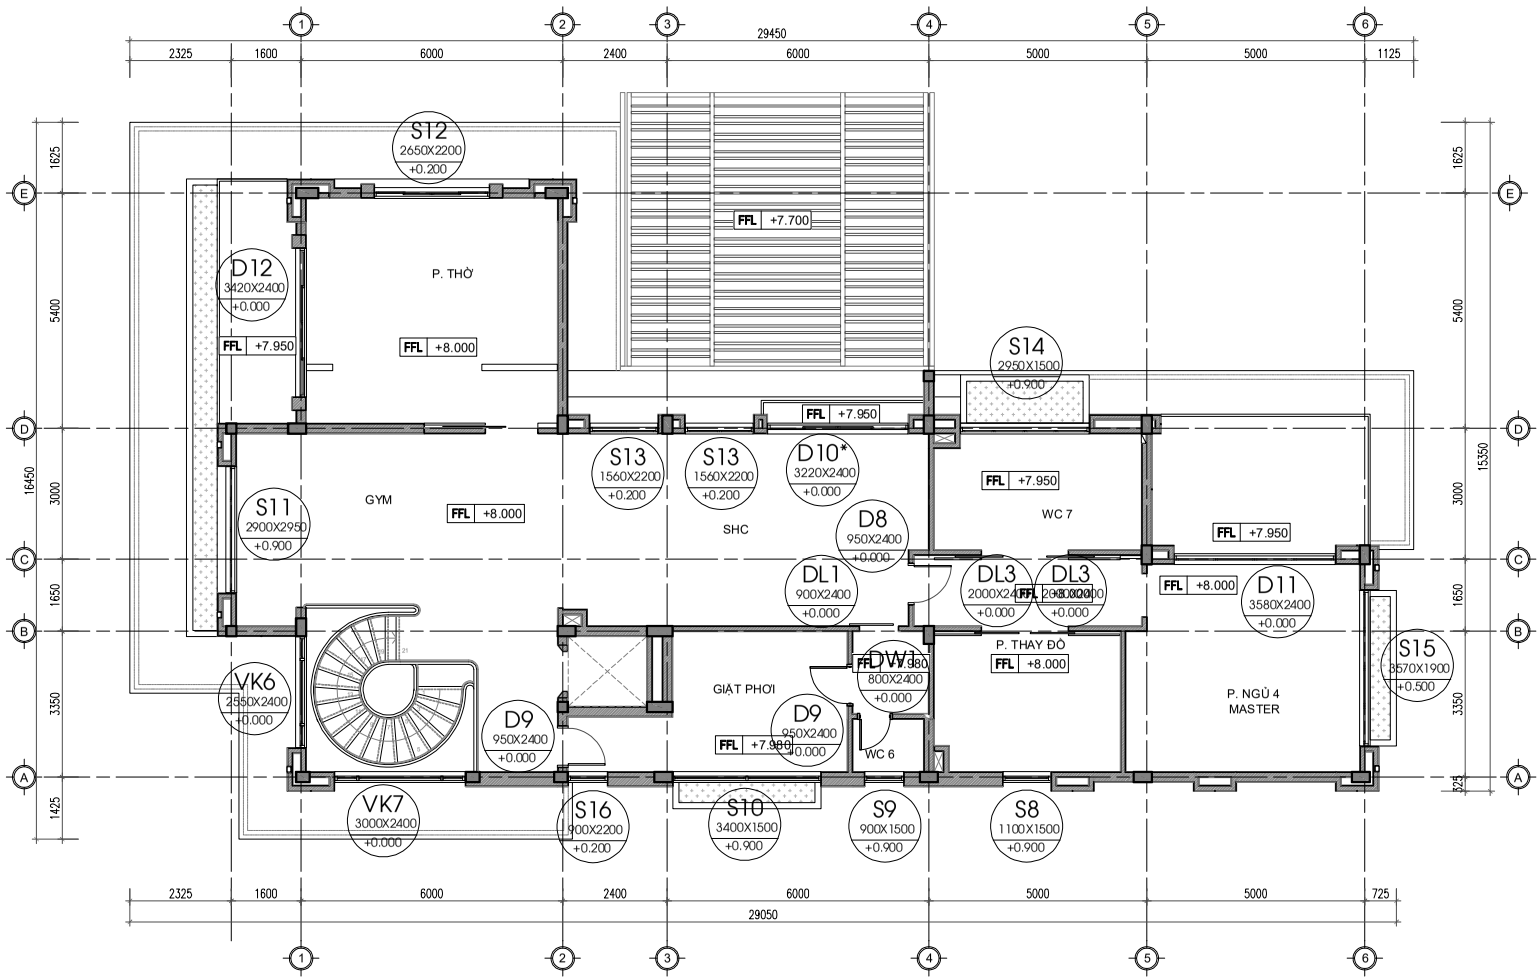

MẶT BẰNG ĐỊNH VỊ CỬA TẦNG 3

LẦN	NGÀY	NỘI DUNG SỬA ĐỔI

CHỦ ĐẦU TƯ - PROJECT OWNER:

ANH ĐỨC ANH

TÊN CÔNG TRÌNH - PROJECT:

BIỆT THỰ VƯỜN

HẠNG MỤC:

KIẾN TRÚC

VỊ TRÍ - LOCATION:

TỈNH HẢI PHÒNG

S - HOUSE DESIGN
INTERIOR DESIGN - CONSTRUCTION

CÔNG TY CỔ PHẦN
S-HOUSE VIỆT NAM
ĐỊA CHỈ: D49 LK7 Ô SỐ 1, KHU ĐÔ THỊ MỚI HAI BÊN ĐƯỜNG LÊ TRỌNG TẤN, PHƯỜNG DƯƠNG NỘI, THÀNH PHỐ HÀ NỘI.
TEL: 0966.005.060
WWW.NHADEPSHOUSE.COM

GIÁM ĐỐC:
DIRECTOR:

GĐ. NGUYỄN VĂN SANG

CHỦ TRÌ KIẾN TRÚC :
PRIMARY ARCHITECT:

KTS.TRƯƠNG QUANG NHẬT

CHỦ TRÌ KẾT CẤU
STRUCTURAL DESIGNER:

KS. ĐỖ MINH KHUÊ

THIẾT KẾ
DESIGNED BY:

KTS. NGUYỄN QUỐC BẢO


TÊN BẢN VẼ:
DRAWING NAME:

MẶT BẰNG ĐỊNH VỊ CỬA TẦNG 3

TỶ LỆ - SCALE:	BẢN VẼ SỐ:
1/70	KT- 47
TÊN FILE - PATH FILE:	
.....	

GHI CHÚ/NOTE:

- Kích thước trên bản vẽ phải được kiểm tra thực tế tại công trình, nếu có sai lệch kích thước tại hiện trường phải báo thiết kế kịp thời để trao đổi phương án xử lý. Người thiết kế sẽ không chịu trách nhiệm kích thước tại công trình.
- Bản vẽ & thiết kế thuộc quyền sở hữu của Công ty CP S-House, không được sao chép nếu không có sự chấp thuận từ S-House.
- Hướng cửa xem trên mặt bằng định vị cửa

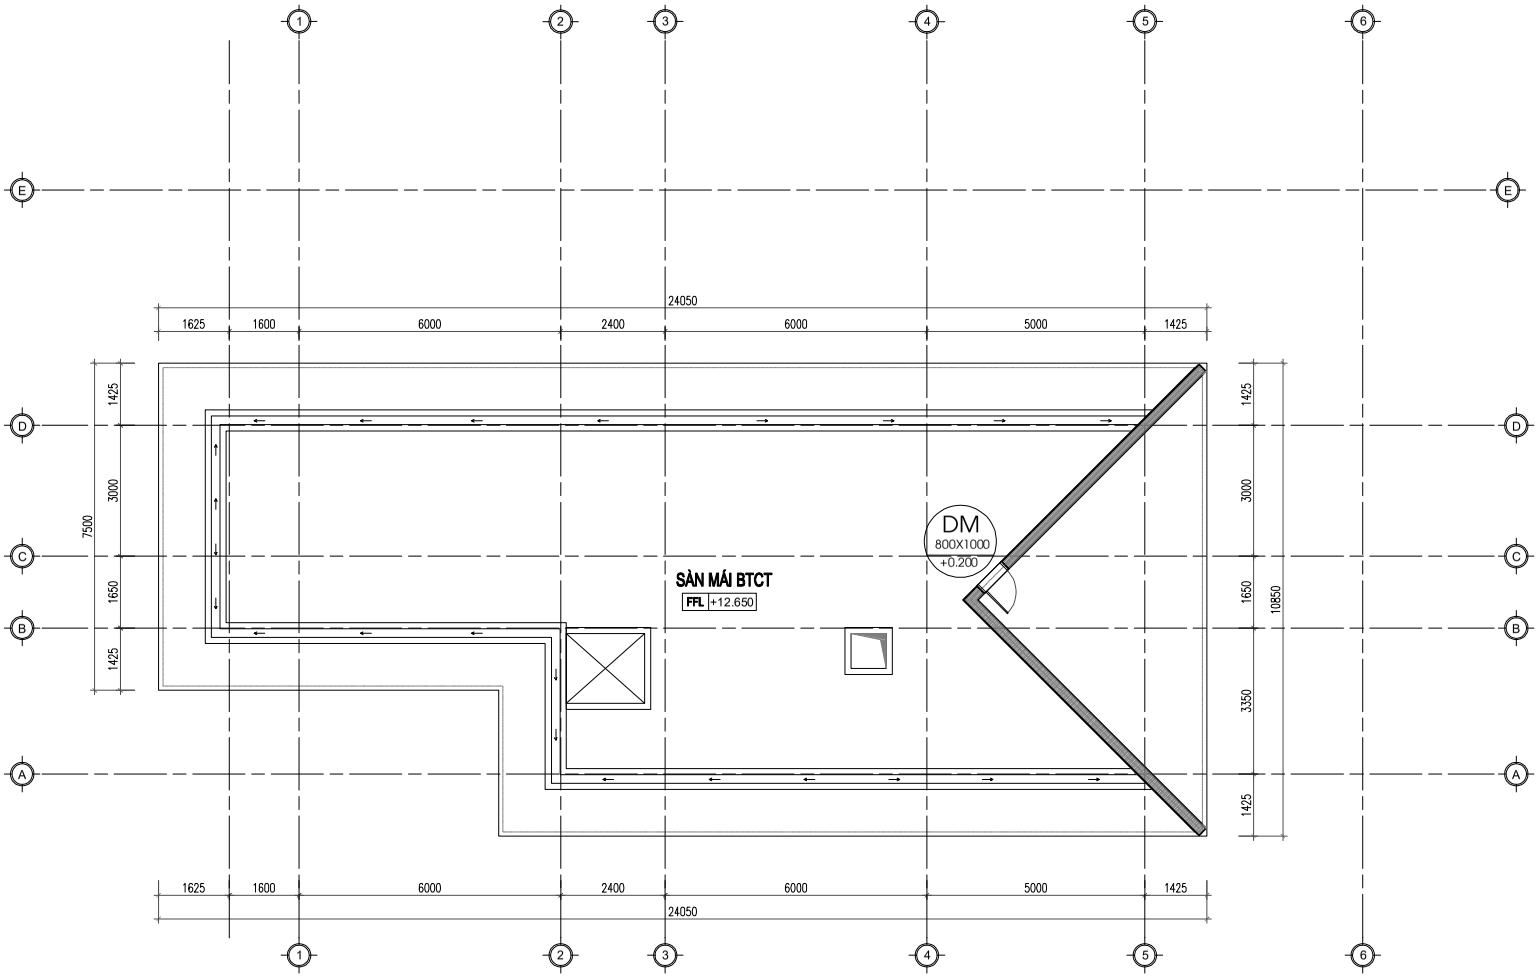

MẶT BẰNG ĐỊNH VỊ CỬA TẦNG MÁI

LẦN	NGÀY	NỘI DUNG SỬA ĐỔI

CHỦ ĐẦU TƯ - PROJECT OWNER:

ANH ĐỨC ANH

TÊN CÔNG TRÌNH - PROJECT:

BIỆT THỰ VƯỜN

HẠNG MỤC:

KIẾN TRÚC

VỊ TRÍ - LOCATION:

TỈNH HẢI PHÒNG

S - HOUSE DESIGN
INTERIOR DESIGN - CONSTRUCTION

CÔNG TY CỔ PHẦN
S-HOUSE VIỆT NAM
ĐỊA CHỈ: D49 LK7 Ô SỐ 1, KHU ĐÔ THỊ MỚI HAI BÊN ĐƯỜNG LÊ TRỌNG TẤN, PHƯỜNG DƯƠNG NỘI, THÀNH PHỐ HÀ NỘI.
TEL: 0966.005.060
WWW.NHADEPSHOUSE.COM

GIÁM ĐỐC:
DIRECTOR:

GĐ. NGUYỄN VĂN SANG

CHỦ TRÌ KIẾN TRÚC :
PRIMARY ARCHITECT:

KTS.TRƯƠNG QUANG NHẬT

CHỦ TRÌ KẾT CẤU
STRUCTURAL DESIGNER:

KS. ĐỖ MINH KHUÊ

THIẾT KẾ
DESIGNED BY:

KTS. NGUYỄN QUỐC BẢO


TÊN BẢN VẼ:
DRAWING NAME:

MẶT BẰNG ĐỊNH VỊ CỬA TẦNG MÁI


TỶ LỆ - SCALE:	BẢN VẼ SỐ:
1/70	KT- 48
TÊN FILE - PATH FILE:	
.....	

GHI CHÚ/NOTE:

- Kích thước trên bản vẽ phải được kiểm tra thực tế tại công trình, nếu có sai lệch kích thước tại hiện trường phải báo thiết kế kịp thời để trao đổi phương án xử lý. Người thiết kế sẽ không chịu trách nhiệm kích thước tại công trình.
- Bản vẽ & thiết kế thuộc quyền sở hữu của Công ty CP S-House, không được sao chép nếu không có sự chấp thuận từ S-House.
- Hướng cửa xem trên mặt bằng định vị cửa

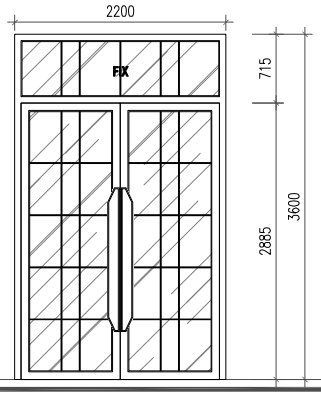



Bên trong

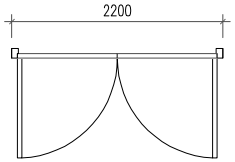


Bên ngoài

D1	QUY CÁCH	CỬA ĐI KHUNG NHÔM MÀU ĐỒNG KÍNH 2 CÁNH MỞ + Ô KÍNH FIX	
	KÍCH THƯỚC	2200X3600 mm	KT LỖ BAN: 2070x2885 mm
CỬA ĐI	SỐ LƯỢNG	01	

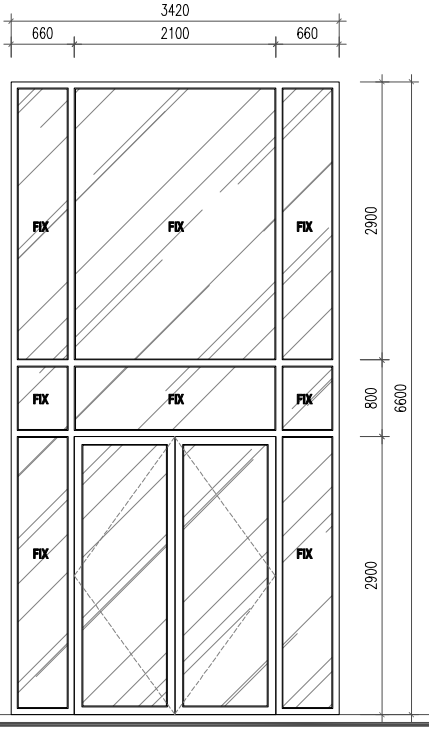

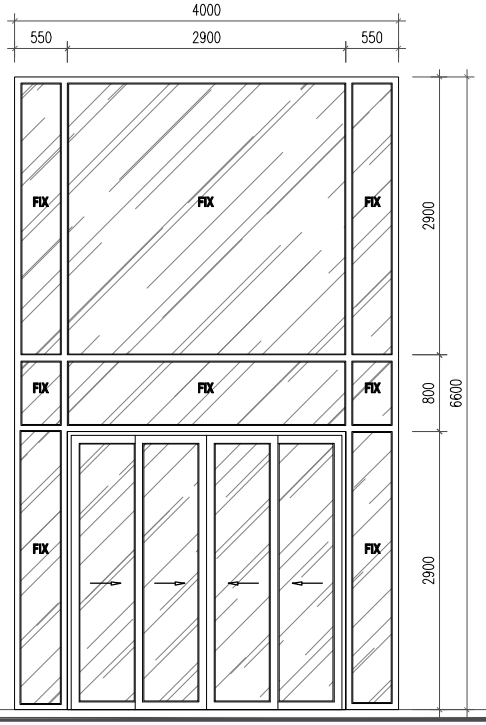


Bên trong

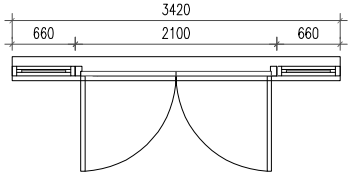

Bên ngoài

D2	QUY CÁCH	CỬA ĐI KHUNG NHÔM KÍNH 2 CÁNH MỞ + Ô KÍNH FIX	
	KÍCH THƯỚC	3420X6600 mm	KT LỖ BAN: 2100X2900 mm
CỬA ĐI	SỐ LƯỢNG	01	

Bên trong

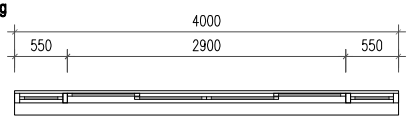

Bên ngoài

D6	QUY CÁCH	CỬA ĐI KHUNG NHÔM KÍNH 4 CÁNH LÙA + Ô KÍNH FIX	
	KÍCH THƯỚC	4000X6600 mm	KT LỖ BAN: 2900X2900 mm
CỬA ĐI	SỐ LƯỢNG	01	

GHI CHÚ: TRƯỚC KHI GIA CÔNG CỬA CẦN KIỂM TRA KĨ KÍCH THƯỚC THỰC TẾ, NẾU CÓ SAI LỆCH CẦN BÁO NGAY CHO ĐƠN VỊ THIẾT KẾ ĐỂ KỊP THỜI XỬ LÝ

LẦN	NGÀY	NỘI DUNG SỬA ĐỔI

CHỦ ĐẦU TƯ - PROJECT OWNER:

ANH ĐỨC ANH

TÊN CÔNG TRÌNH - PROJECT:

BIỆT THỰ VƯỜN

HẠNG MỤC:

KIẾN TRÚC

VỊ TRÍ - LOCATION:

TỈNH HẢI PHÒNG

S - HOUSE DESIGN
INTERIOR DESIGN - CONSTRUCTION

CÔNG TY CỔ PHẦN
S-HOUSE VIỆT NAM
ĐỊA CHỈ: D49 LK7 Ô SỐ 1, KHU ĐÔ THỊ MỚI HAI BÊN ĐƯỜNG LÊ TRỌNG TẤN, PHƯỜNG DƯƠNG NỘI, THÀNH PHỐ HÀ NỘI.
TEL: 0966.005.050
WWW.NHADEPSHOUSE.COM

GIÁM ĐỐC:
DIRECTOR:

GĐ. NGUYỄN VĂN SANG

CHỦ TRÌ KIẾN TRÚC :
PRIMARY ARCHITECT:

KTS.TRƯƠNG QUANG NHẬT

CHỦ TRÌ KẾT CẤU
STRUCTURAL DESIGNER:

KS. ĐỖ MINH KHUÊ

THIẾT KẾ
DESIGNED BY:

KTS. NGUYỄN QUỐC BẢO


TÊN BẢN VẼ:
DRAWING NAME:


CHI TIẾT CỬA

TỶ LỆ - SCALE:	BẢN VẼ SỐ:
1/50	KT- 49
TÊN FILE - PATH FILE:	


GHI CHÚ/NOTE:

- Kích thước trên bản vẽ phải được kiểm tra thực tế tại công trình, nếu có sai lệch kích thước tại hiện trường phải báo thiết kế kịp thời để trao đổi phương án xử lý. Người thiết kế sẽ không chịu trách nhiệm kích thước tại công trình.
- Bản vẽ & thiết kế thuộc quyền sở hữu của Công ty CP S-House, không được sao chép nếu không có sự chấp thuận từ S-House.
- Hướng cửa xem trên mặt bằng định vị cửa

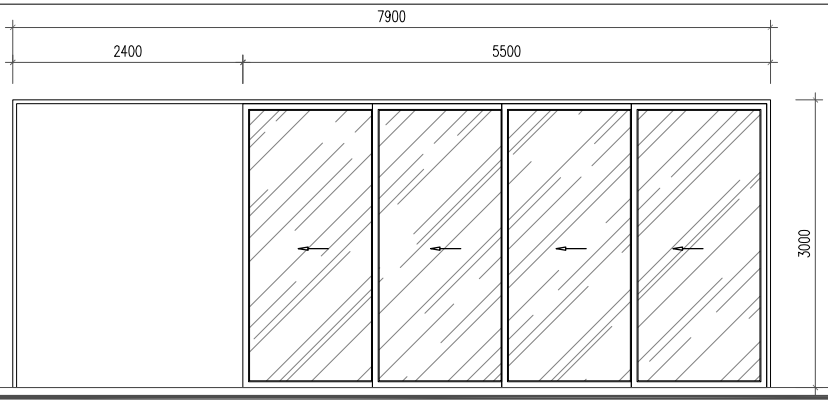

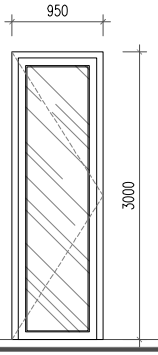


Bên ngoài

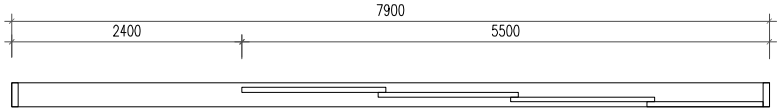

Bên trong


D4	QUY CÁCH	CỬA ĐI KHUNG NHÔM KÍNH 4 CÁNH LÙA	
	KÍCH THƯỚC	5500X3000 mm	KT LỖ BAN: 2935X5435 mm
CỬA ĐI	SỐ LƯỢNG	01	


Bên ngoài

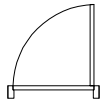


Bên trong

D5	QUY CÁCH	CỬA ĐI KHUNG NHÔM KÍNH 1 CÁNH MỞ	
	KÍCH THƯỚC	950X3000 mm	KT LỖ BAN: 820X2935 mm
CỬA ĐI	SỐ LƯỢNG	01	

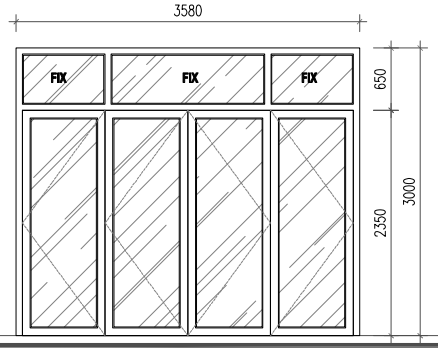

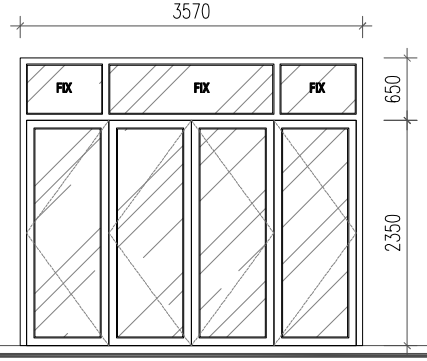


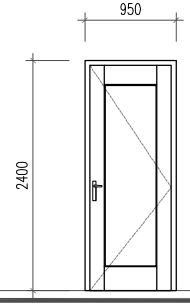

Bên ngoài



Bên trong

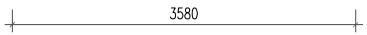


D6	QUY CÁCH	CỬA ĐI KHUNG NHÔM KÍNH 4 CÁNH MỞ + Ô KÍNH FIX	
	KÍCH THƯỚC	3580X3000 mm	KT LỖ BAN: 3450X2350 mm
CỬA ĐI	SỐ LƯỢNG	01	

Bên ngoài




Bên trong

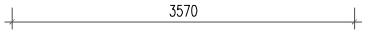

D7	QUY CÁCH	CỬA ĐI KHUNG NHÔM KÍNH 4 CÁNH MỞ + Ô KÍNH FIX	
	KÍCH THƯỚC	3570X3000 mm	KT LỖ BAN: 3440X2350 mm
CỬA ĐI	SỐ LƯỢNG	01	

Bên trong

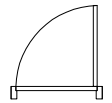

Bên ngoài

D8	QUY CÁCH	CỬA ĐI GỖ 1 CÁNH MỞ - XEM CHI TIẾT BV TRIỂN KHAI NỘI THẤT	
	KÍCH THƯỚC	950X2400 mm	KT LỖ BAN: 830X2340 mm
CỬA ĐI	SỐ LƯỢNG	04	

GHI CHÚ: TRƯỚC KHI GIA CÔNG CỬA CẦN KIỂM TRA KĨ KÍCH THƯỚC THỰC TẾ, NẾU CÓ SAI LỆCH CẦN BÁO NGAY CHO ĐƠN VỊ THIẾT KẾ ĐỂ KỊP THỜI XỬ LÝ

LẦN	NGÀY	NỘI DUNG SỬA ĐỔI

CHỦ ĐẦU TƯ - PROJECT OWNER:

ANH ĐỨC ANH

TÊN CÔNG TRÌNH - PROJECT:

BIỆT THỰ VƯỜN

HẠNG MỤC:

KIẾN TRÚC

VỊ TRÍ - LOCATION:

TỈNH HẢI PHÒNG

S - HOUSE DESIGN
INTERIOR DESIGN - CONSTRUCTION

CÔNG TY CỔ PHẦN
S-HOUSE VIỆT NAM
ĐỊA CHỈ: D49 LK7 Ô SỐ 1, KHU ĐÔ THỊ MỚI HAI BÊN ĐƯỜNG LÊ TRỌNG TẤN, PHƯỜNG DƯƠNG NỘI, THÀNH PHỐ HÀ NỘI.
TEL: 0966.005.060
WWW.NHADEPSHOUSE.COM

GIÁM ĐỐC:
DIRECTOR:

GĐ. NGUYỄN VĂN SANG

CHỦ TRÌ KIẾN TRÚC :
PRIMARY ARCHITECT:

KTS.TRƯƠNG QUANG NHẬT

CHỦ TRÌ KẾT CẤU
STRUCTURAL DESIGNER:

KS. ĐỖ MINH KHUÊ

THIẾT KẾ
DESIGNED BY:

KTS. NGUYỄN QUỐC BẢO

TÊN BẢN VẼ:
DRAWING NAME:

CHI TIẾT CỬA


TỶ LỆ - SCALE: 1/20

BẢN VẼ SỐ: KT- 50


TÊN FILE - PATH FILE: .....

GHI CHÚ/NOTE:

- Kích thước trên bản vẽ phải được kiểm tra thực tế tại công trình, nếu có sai lệch kích thước tại hiện trường phải báo thiết kế kịp thời để trao đổi phương án xử lý. Người thiết kế sẽ không chịu trách nhiệm kích thước tại công trình.
- Bản vẽ & thiết kế thuộc quyền sở hữu của Công ty CP S-House, không được sao chép nếu không có sự chấp thuận từ S-House.
- Hướng cửa xem trên mặt bằng định vị cửa

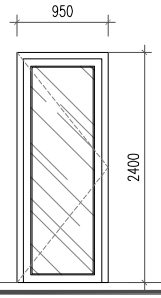


Bên ngoài

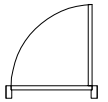

Bên trong

D9	QUY CÁCH	CỬA ĐI KHUNG NHÔM KÍNH 1 CÁNH MỞ	
	KÍCH THƯỚC	950X2400 mm	KT LỖ BAN: 820X2335 mm
CỬA ĐI	SỐ LƯỢNG	04	

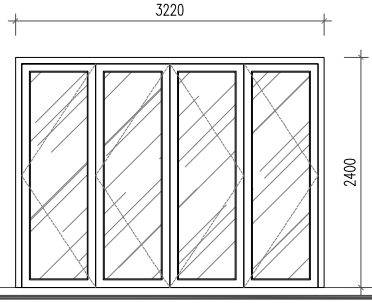


Bên ngoài




Bên trong

D10	QUY CÁCH	CỬA ĐI KHUNG NHÔM KÍNH 4 CÁNH MỞ	
	KÍCH THƯỚC	3220X2400 mm	KT LỖ BAN: 3090X2335 mm
CỬA ĐI	SỐ LƯỢNG	01	

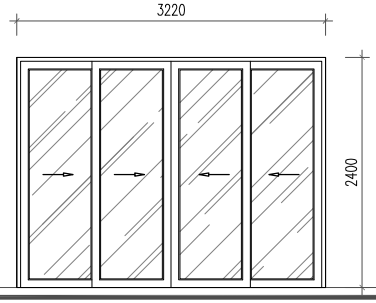


Bên ngoài

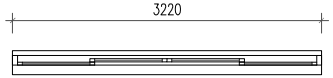


Bên trong

D10*	QUY CÁCH	CỬA ĐI KHUNG NHÔM KÍNH 4 CÁNH LÙA	
	KÍCH THƯỚC	3220X2400 mm	
CỬA ĐI	SỐ LƯỢNG	01	

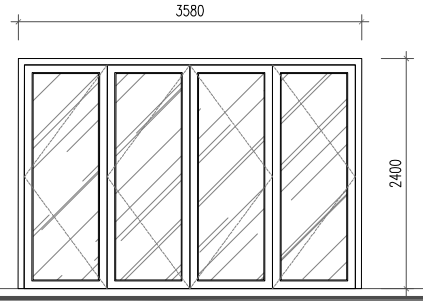


Bên ngoài

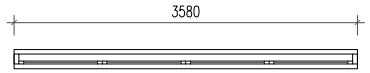


Bên trong

D11	QUY CÁCH	CỬA ĐI KHUNG NHÔM KÍNH 4 CÁNH MỞ	
	KÍCH THƯỚC	3580x2400 mm	KT LỖ BAN: 3450x2335 mm
CỬA ĐI	SỐ LƯỢNG	02	

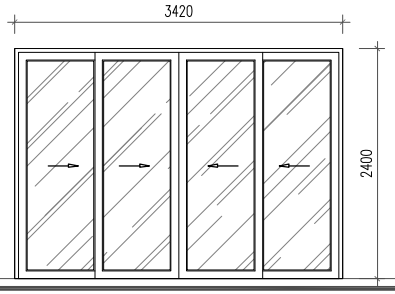


Bên ngoài

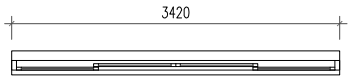


Bên trong

D12	QUY CÁCH	CỬA ĐI KHUNG NHÔM KÍNH 4 CÁNH LÙA	
	KÍCH THƯỚC	3420X2400 mm	KT LỖ BAN: 3340X2360 mm
CỬA ĐI	SỐ LƯỢNG	01	

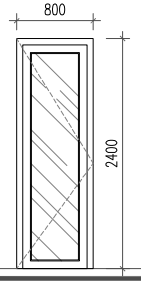

Bên trong

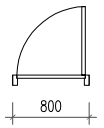

Bên ngoài

DW1	QUY CÁCH	CỬA ĐI KHUNG NHÔM KÍNH 1 CÁNH MỞ	
	KÍCH THƯỚC	800X2400 mm	
CỬA ĐI	SỐ LƯỢNG	02	

GHI CHÚ: TRƯỚC KHI GIA CÔNG CỬA CẦN KIỂM TRA KĨ KÍCH THƯỚC THỰC TẾ, NẾU CÓ SAI LỆCH CẦN BÁO NGAY CHO ĐƠN VỊ THIẾT KẾ ĐỂ KỊP THỜI XỬ LÝ

LẦN	NGÀY	NỘI DUNG SỬA ĐỔI

CHỦ ĐẦU TƯ - PROJECT OWNER:

ANH ĐỨC ANH

TÊN CÔNG TRÌNH - PROJECT:

BIỆT THỰ VƯỜN

HẠNG MỤC:

KIẾN TRÚC

VỊ TRÍ - LOCATION:

TỈNH HẢI PHÒNG

S - HOUSE DESIGN
INTERIOR DESIGN - CONSTRUCTION

CÔNG TY CỔ PHẦN
S-HOUSE VIỆT NAM
ĐỊA CHỈ: D49 LK7 Ô SỐ 1, KHU ĐÔ THỊ MỚI HAI BÊN ĐƯỜNG LÊ TRỌNG TẤN, PHƯỜNG DƯƠNG NỘI, THÀNH PHỐ HÀ NỘI.
TEL: 0966.005.060
WWW.NHADEPSHOUSE.COM

GIÁM ĐỐC:
DIRECTOR:

GĐ. NGUYỄN VĂN SANG

CHỦ TRÌ KIẾN TRÚC :
PRIMARY ARCHITECT:

KTS.TRƯƠNG QUANG NHẬT

CHỦ TRÌ KẾT CẤU
STRUCTURAL DESIGNER:

KS. ĐỖ MINH KHUÊ

THIẾT KẾ
DESIGNED BY:

KTS. NGUYỄN QUỐC BẢO

TÊN BẢN VẼ:
DRAWING NAME:


CHI TIẾT CỬA

TỶ LỆ - SCALE: 1/20


BẢN VẼ SỐ: KT- 51

TÊN FILE - PATH FILE: .....

GHI CHÚ/NOTE:
- Kích thước trên bản vẽ phải được kiểm tra thực tế tại công trình, nếu có sai lệch kích thước tại hiện trường phải báo thiết kế kịp thời để trao đổi phương án xử lý. Người thiết kế sẽ không chịu trách nhiệm kích thước tại công trình.
- Bản vẽ & thiết kế thuộc quyền sở hữu của Công ty CP S-House, không được sao chép nếu không có sự chấp thuận từ S-House.
- Hướng cửa xem trên mặt bằng định vị cửa

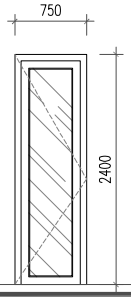


Bên trong

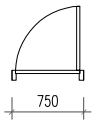


Bên ngoài

DW2	QUY CÁCH	CỬA ĐI KHUNG NHÔM KÍNH 1 CÁNH MỞ
	KÍCH THƯỚC	750X2400 mm
CỬA ĐI	SỐ LƯỢNG	01

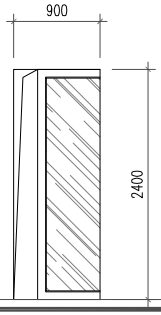


Bên ngoài

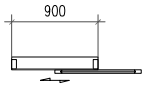


Bên trong

DL1	QUY CÁCH	CỬA ĐI KHUNG NHÔM KÍNH 1 CÁNH LÙA
	KÍCH THƯỚC	900X2400 mm
CỬA ĐI	SỐ LƯỢNG	02

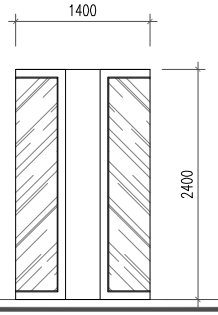


Bên ngoài

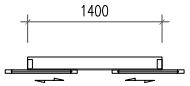


Bên trong

DL2	QUY CÁCH	CỬA ĐI KHUNG NHÔM KÍNH 2 CÁNH LÙA
	KÍCH THƯỚC	1400X2400 mm
CỬA ĐI	SỐ LƯỢNG	01

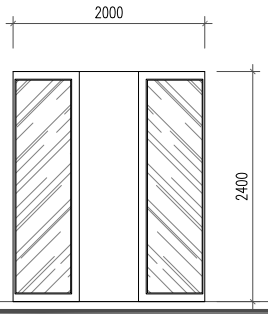


Bên ngoài

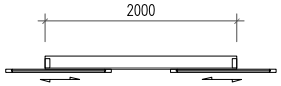


Bên trong

DL3	QUY CÁCH	CỬA ĐI KHUNG NHÔM KÍNH 2 CÁNH LÙA
	KÍCH THƯỚC	2000x2400 mm
CỬA ĐI	SỐ LƯỢNG	03

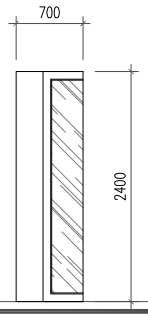


Bên ngoài

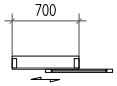


Bên trong

DL4	QUY CÁCH	CỬA ĐI KHUNG NHÔM KÍNH 1 CÁNH LÙA
	KÍCH THƯỚC	700X2400 mm
CỬA ĐI	SỐ LƯỢNG	01

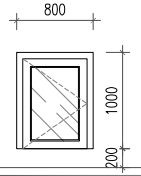

Bên trong

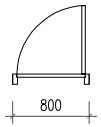

Bên ngoài

DM	QUY CÁCH	CỬA ĐI KHUNG NHÔM KÍNH 1 CÁNH MỞ
	KÍCH THƯỚC	800X1000 mm
CỬA ĐI	SỐ LƯỢNG	01

GHI CHÚ: TRƯỚC KHI GIA CÔNG CỬA CẦN KIỂM TRA KĨ KÍCH THƯỚC THỰC TẾ, NẾU CÓ SAI LỆCH CẦN BÁO NGAY CHO ĐƠN VỊ THIẾT KẾ ĐỂ KỊP THỜI XỬ LÝ

LẦN	NGÀY	NỘI DUNG SỬA ĐỔI

CHỦ ĐẦU TƯ - PROJECT OWNER:

ANH ĐỨC ANH

TÊN CÔNG TRÌNH - PROJECT:

BIỆT THỰ VƯỜN

HẠNG MỤC:

KIẾN TRÚC

VỊ TRÍ - LOCATION:

TỈNH HẢI PHÒNG

S - HOUSE DESIGN
INTERIOR DESIGN - CONSTRUCTION

CÔNG TY CỔ PHẦN
S-HOUSE VIỆT NAM
ĐỊA CHỈ: D49 LK7 Ô SỐ 1, KHU ĐÔ THỊ MỚI HAI BÊN ĐƯỜNG LÊ TRỌNG TẤN, PHƯỜNG DƯƠNG NỘI, THÀNH PHỐ HÀ NỘI.
TEL: 0966.005.060
WWW.NHADEPSHOUSE.COM

GIÁM ĐỐC:
DIRECTOR:

GĐ. NGUYỄN VĂN SANG

CHỦ TRÌ KIẾN TRÚC :
PRIMARY ARCHITECT:

KTS.TRƯƠNG QUANG NHẬT

CHỦ TRÌ KẾT CẤU
STRUCTURAL DESIGNER:

KS. ĐỖ MINH KHUÊ

THIẾT KẾ
DESIGNED BY:

KTS. NGUYỄN QUỐC BẢO

TÊN BẢN VẼ:
DRAWING NAME:

CHI TIẾT CỬA


TỶ LỆ - SCALE: 1/20


BẢN VẼ SỐ: KT- 52


TÊN FILE - PATH FILE: .....

GHI CHÚ/NOTE:


- Kích thước trên bản vẽ phải được kiểm tra thực tế tại công trình, nếu có sai lệch kích thước tại hiện trường phải báo thiết kế kịp thời để trao đổi phương án xử lý. Người thiết kế sẽ không chịu trách nhiệm kích thước tại công trình.
- Bản vẽ & thiết kế thuộc quyền sở hữu của Công ty CP S-House, không được sao chép nếu không có sự chấp thuận từ S-House.
- Hướng cửa xem trên mặt bằng định vị cửa

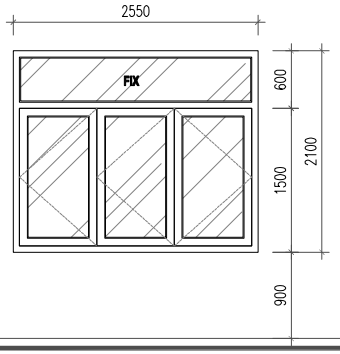

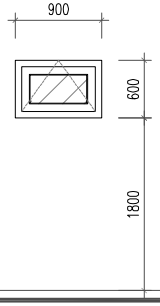

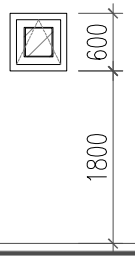


Bên ngoài

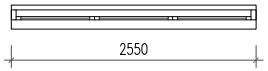

Bên trong

S1	QUY CÁCH	CỬA SỔ KHUNG NHÔM KÍNH 3 CÁNH MỞ + Ô KÍNH FIX
	KÍCH THƯỚC	2550X2100 mm
CỬA SỔ	SỐ LƯỢNG	01

Bên trong

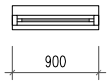

Bên ngoài


S2	QUY CÁCH	CỬA SỔ KHUNG NHÔM KÍNH 1 CÁNH HẤT
	KÍCH THƯỚC	900X600 mm
CỬA SỔ	SỐ LƯỢNG	01


Bên trong




Bên ngoài


S2	QUY CÁCH	CỬA SỔ KHUNG NHÔM KÍNH 1 CÁNH HẤT
	KÍCH THƯỚC	590X600 mm
CỬA SỔ	SỐ LƯỢNG	01

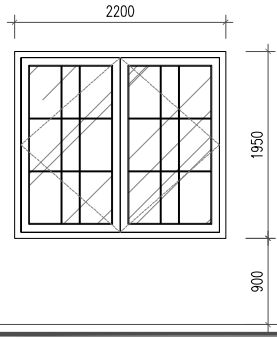

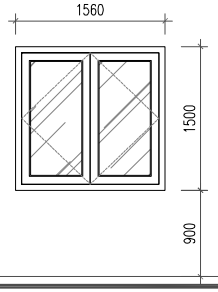

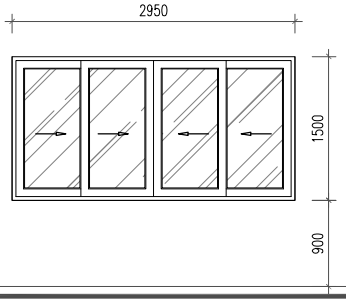


Bên ngoài

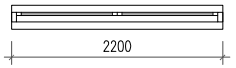

Bên trong

S4	QUY CÁCH	CỬA SỔ KHUNG NHÔM MÀU ĐỒNG KÍNH 2 CÁNH MỞ
	KÍCH THƯỚC	2200X1950 mm
CỬA SỔ	SỐ LƯỢNG	01


Bên trong

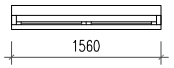

Bên ngoài

S5	QUY CÁCH	CỬA SỔ KHUNG NHÔM KÍNH 2 CÁNH MỞ
	KÍCH THƯỚC	1560X1500 mm
CỬA SỔ	SỐ LƯỢNG	02

Bên trong

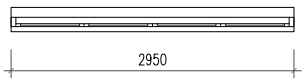

Bên ngoài

S6	QUY CÁCH	CỬA SỔ KHUNG NHÔM KÍNH 4 CÁNH LÙA
	KÍCH THƯỚC	2950X1500 mm
CỬA SỔ	SỐ LƯỢNG	01

GHI CHÚ: TRƯỚC KHI GIA CÔNG CỬA CẦN KIỂM TRA KĨ KÍCH THƯỚC THỰC TẾ, NẾU CÓ SAI LỆCH CẦN BÁO NGAY CHO ĐƠN VỊ THIẾT KẾ ĐỂ KỊP THỜI XỬ LÝ

LẦN	NGÀY	NỘI DUNG SỬA ĐỔI

CHỦ ĐẦU TƯ - PROJECT OWNER:
ANH ĐỨC ANH

TÊN CÔNG TRÌNH - PROJECT:
BIỆT THỰ VƯỜN

HẠNG MỤC:
KIẾN TRÚC

VỊ TRÍ - LOCATION:
TỈNH HẢI PHÒNG

S - HOUSE DESIGN
INTERIOR DESIGN - CONSTRUCTION

CÔNG TY CỔ PHẦN
S-HOUSE VIỆT NAM
ĐỊA CHỈ: D49 LK7 Ô SỐ 1, KHU ĐÔ THỊ MỚI HAI BÊN ĐƯỜNG LÊ TRỌNG TẤN, PHƯỜNG DƯƠNG NỘI, THÀNH PHỐ HÀ NỘI.
TEL: 0966.005.040
WWW.NHADEPSHOUSE.COM

GIÁM ĐỐC:
DIRECTOR:
GĐ. NGUYỄN VĂN SANG

CHỦ TRÌ KIẾN TRÚC :
PRIMARY ARCHITECT:
KTS.TRƯƠNG QUANG NHẬT

CHỦ TRÌ KẾT CẤU
STRUCTURAL DESIGNER:
KS. ĐỖ MINH KHUÊ

THIẾT KẾ
DESIGNED BY:
KTS. NGUYỄN QUỐC BẢO


TÊN BẢN VẼ:
DRAWING NAME:
CHI TIẾT CỬA


TỶ LỆ - SCALE: 1/20


BẢN VẼ SỐ: KT- 53

TÊN FILE - PATH FILE: .....


GHI CHÚ/NOTE:
- Kích thước trên bản vẽ phải được kiểm tra thực tế tại công trình, nếu có sai lệch kích thước tại hiện trường phải báo thiết kế kịp thời để trao đổi phương án xử lý. Người thiết kế sẽ không chịu trách nhiệm kích thước tại công trình.
- Bản vẽ & thiết kế thuộc quyền sở hữu của Công ty CP S-House, không được sao chép nếu không có sự chấp thuận từ S-House.
- Hướng cửa xem trên mặt bằng định vị cửa

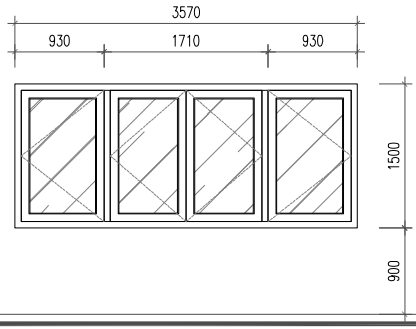

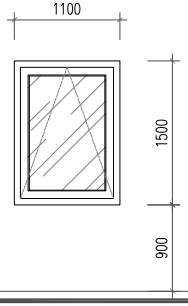

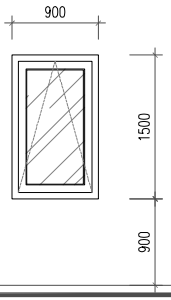


Bên trong

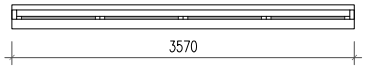


Bên ngoài

S7	QUY CÁCH	CỬA SỔ KHUNG NHÔM KÍNH 4 CÁNH MỞ
	KÍCH THƯỚC	3570X1500 mm
CỬA SỔ	SỐ LƯỢNG	01

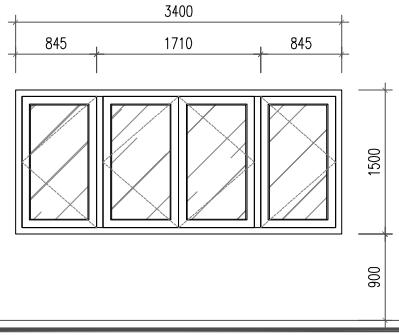


Bên trong

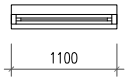


Bên ngoài

S8	QUY CÁCH	CỬA SỔ KHUNG NHÔM KÍNH 1 CÁNH HẤT
	KÍCH THƯỚC	1100X1500 mm
CỬA SỔ	SỐ LƯỢNG	02

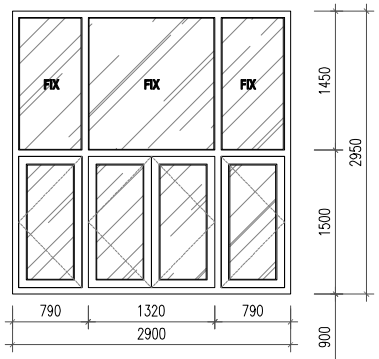


Bên trong

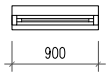


Bên ngoài

S9	QUY CÁCH	CỬA SỔ KHUNG NHÔM KÍNH 1 CÁNH HẤT
	KÍCH THƯỚC	590X600 mm
CỬA SỔ	SỐ LƯỢNG	03

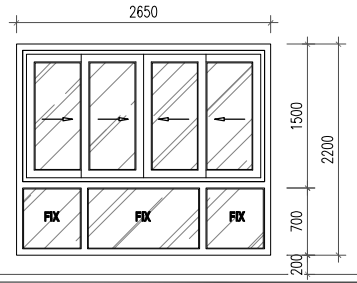


Bên trong

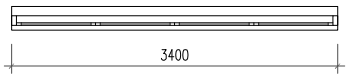

Bên ngoài

S10	QUY CÁCH	CỬA SỔ KHUNG NHÔM KÍNH 4 CÁNH MỞ
	KÍCH THƯỚC	3400X1500 mm
CỬA SỔ	SỐ LƯỢNG	02


Bên trong

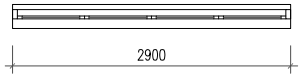

Bên ngoài

S11	QUY CÁCH	CỬA SỔ KHUNG NHÔM KÍNH 4 CÁNH MỞ + Ô KÍNH FIX
	KÍCH THƯỚC	2900X2950 mm
CỬA SỔ	SỐ LƯỢNG	01

Bên trong

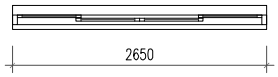

Bên ngoài

S12	QUY CÁCH	CỬA SỔ KHUNG NHÔM KÍNH 4 CÁNH LÙA + Ô KÍNH FIX
	KÍCH THƯỚC	2650X2200 mm
CỬA SỔ	SỐ LƯỢNG	01

GHI CHÚ: TRƯỚC KHI GIA CÔNG CỬA CẦN KIỂM TRA KĨ KÍCH THƯỚC THỰC TẾ, NẾU CÓ SAI LỆCH CẦN BÁO NGAY CHO ĐƠN VỊ THIẾT KẾ ĐỂ KỊP THỜI XỬ LÝ

LẦN	NGÀY	NỘI DUNG SỬA ĐỔI

CHỦ ĐẦU TƯ - PROJECT OWNER:

ANH ĐỨC ANH

TÊN CÔNG TRÌNH - PROJECT:

BIỆT THỰ VƯỜN

HẠNG MỤC:

KIẾN TRÚC

VỊ TRÍ - LOCATION:

TỈNH HẢI PHÒNG

S - HOUSE DESIGN
INTERIOR DESIGN - CONSTRUCTION

CÔNG TY CỔ PHẦN
S-HOUSE VIỆT NAM
ĐỊA CHỈ: D49 LK7 Ô SỐ 1, KHU ĐÔ THỊ MỚI HAI BÊN ĐƯỜNG LÊ TRỌNG TẤN, PHƯỜNG DƯƠNG NỘI, THÀNH PHỐ HÀ NỘI.
TEL: 0966.005.040
WWW.NHADEPSHOUSE.COM

GIÁM ĐỐC:
DIRECTOR:

GĐ. NGUYỄN VĂN SANG

CHỦ TRÌ KIẾN TRÚC :
PRIMARY ARCHITECT:

KTS.TRƯƠNG QUANG NHẬT

CHỦ TRÌ KẾT CẤU
STRUCTURAL DESIGNER:

KS. ĐỖ MINH KHUÊ

THIẾT KẾ
DESIGNED BY:


KTS. NGUYỄN QUỐC BÁO


TÊN BẢN VẼ:
DRAWING NAME:


CHI TIẾT CỬA

TỶ LỆ - SCALE:	BẢN VẼ SỐ:
1/20	KT- 54
TÊN FILE - PATH FILE:	


GHI CHÚ/NOTE:
- Kích thước trên bản vẽ phải được kiểm tra thực tế tại công trình, nếu có sai lệch kích thước tại hiện trường phải báo thiết kế kịp thời để trao đổi phương án xử lý. Người thiết kế sẽ không chịu trách nhiệm kích thước tại công trình.
- Bản vẽ & thiết kế thuộc quyền sở hữu của Công ty CP S-House, không được sao chép nếu không có sự chấp thuận từ S-House.
- Hướng cửa xem trên mặt bằng định vị cửa

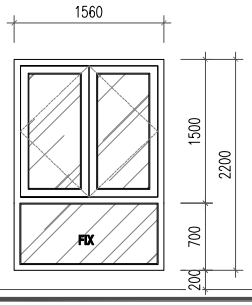

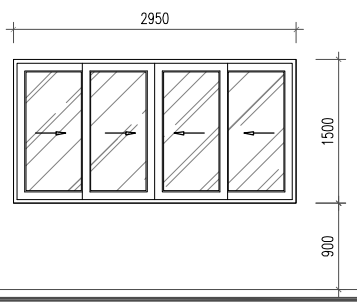

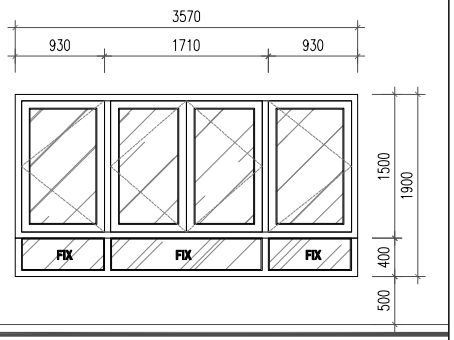


Bên trong

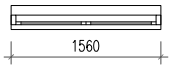

Bên ngoài

S13	QUY CÁCH	CỬA SỔ KHUNG NHÔM KÍNH 2 CÁNH MỞ + Ô KÍNH FIX
	KÍCH THƯỚC	1560X2200 mm
CỬA SỔ	SỐ LƯỢNG	02


Bên trong

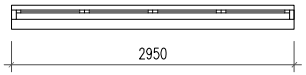

Bên ngoài


S14	QUY CÁCH	CỬA SỔ KHUNG NHÔM KÍNH 4 CÁNH LÙA + Ô KÍNH FIX
	KÍCH THƯỚC	1100X1500 mm
CỬA SỔ	SỐ LƯỢNG	01

Bên trong

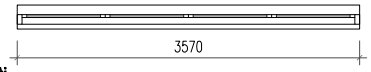


Bên ngoài

S15	QUY CÁCH	CỬA SỔ KHUNG NHÔM KÍNH 4 CÁNH MỞ + Ô KÍNH FIX
	KÍCH THƯỚC	3570X1900 mm
CỬA SỔ	SỐ LƯỢNG	01

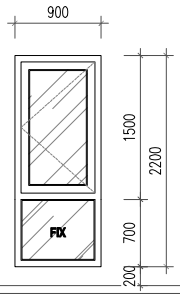

Bên trong

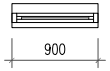

Bên ngoài

S16	QUY CÁCH	CỬA SỔ KHUNG NHÔM KÍNH 1 CÁNH MỞ + Ô KÍNH FIX
	KÍCH THƯỚC	900X2200 mm
CỬA SỔ	SỐ LƯỢNG	01

Bên trong

Bên ngoài

VK1	QUY CÁCH	CỬA SỔ KHUNG NHÔM KÍNH 2 CÁNH MỞ
	KÍCH THƯỚC	2900X2950 mm
VÁCH KÍNH	SỐ LƯỢNG	01

Bên trong

Bên ngoài

S12	QUY CÁCH	CỬA SỔ KHUNG NHÔM KÍNH 4 CÁNH LÙA
	KÍCH THƯỚC	2650X2200 mm
CỬA SỔ	SỐ LƯỢNG	01

GHI CHÚ: TRƯỚC KHI GIA CÔNG CỬA CẦN KIỂM TRA KĨ KÍCH THƯỚC THỰC TẾ, NẾU CÓ SAI LỆCH CẦN BÁO NGAY CHO ĐƠN VỊ THIẾT KẾ ĐỂ KỊP THỜI XỬ LÝ

LẦN	NGÀY	NỘI DUNG SỬA ĐỔI

CHỦ ĐẦU TƯ - PROJECT OWNER:

ANH ĐỨC ANH

TÊN CÔNG TRÌNH - PROJECT:

BIỆT THỰ VƯỜN

HẠNG MỤC:

KIẾN TRÚC

VỊ TRÍ - LOCATION:

TỈNH HẢI PHÒNG

S - HOUSE DESIGN
INTERIOR DESIGN - CONSTRUCTION

CÔNG TY CỔ PHẦN
S-HOUSE VIỆT NAM
ĐỊA CHỈ: D49 LK7 Ô SỐ 1, KHU ĐÔ THỊ MỚI HAI BÊN ĐƯỜNG LÊ TRỌNG TẤN, PHƯỜNG DƯƠNG NỘI, THÀNH PHỐ HÀ NỘI.
TEL: 0966.005.060
WWW.NHADEPSHOUSE.COM

GIÁM ĐỐC:
DIRECTOR:

GĐ. NGUYỄN VĂN SANG

CHỦ TRÌ KIẾN TRÚC :
PRIMARY ARCHITECT:

KTS.TRƯƠNG QUANG NHẬT

CHỦ TRÌ KẾT CẤU
STRUCTURAL DESIGNER:

KS. ĐỖ MINH KHUÊ

THIẾT KẾ
DESIGNED BY:

KTS. NGUYỄN QUỐC BẢO

TÊN BẢN VẼ:
DRAWING NAME:

CHI TIẾT CỬA


TỶ LỆ - SCALE: 1/20


BẢN VẼ SỐ: KT- 55


TÊN FILE - PATH FILE: .....

GHI CHÚ/NOTE:


- Kích thước trên bản vẽ phải được kiểm tra thực tế tại công trình, nếu có sai lệch kích thước tại hiện trường phải báo thiết kế kịp thời để trao đổi phương án xử lý. Người thiết kế sẽ không chịu trách nhiệm kích thước tại công trình.
- Bản vẽ & thiết kế thuộc quyền sở hữu của Công ty CP S-House, không được sao chép nếu không có sự chấp thuận từ S-House.
- Hướng cửa xem trên mặt bằng định vị cửa

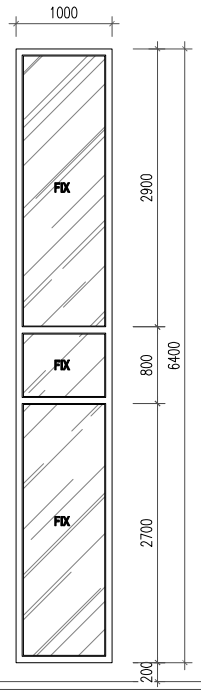

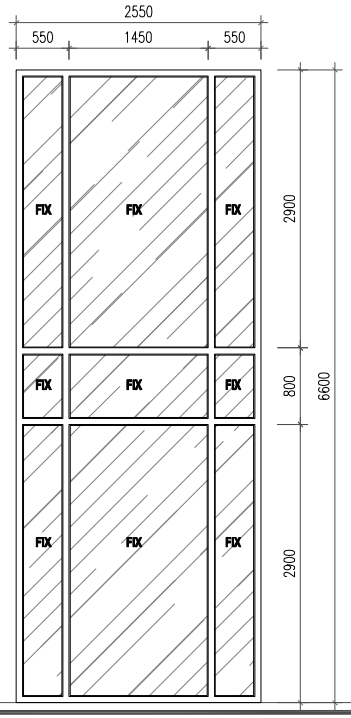

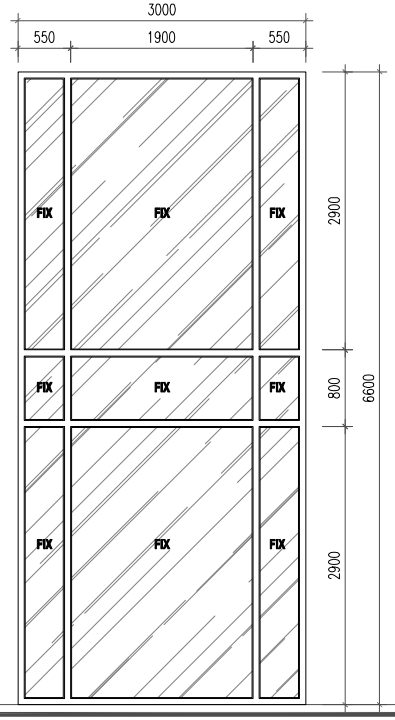


Bên trong

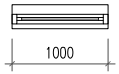

Bên ngoài

VK1	QUY CÁCH	KHUNG NHÔM + Ô KÍNH FIX
	KÍCH THƯỚC	1000X6400 mm
VÁCH KÍNH	SỐ LƯỢNG	02


Bên trong

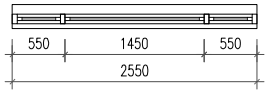

Bên ngoài

VK2	QUY CÁCH	KHUNG NHÔM + Ô KÍNH FIX
	KÍCH THƯỚC	2550X6600 mm
VÁCH KÍNH	SỐ LƯỢNG	01

Bên trong

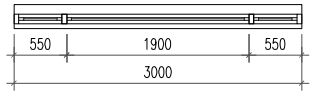

Bên ngoài

VK3	QUY CÁCH	KHUNG NHÔM + Ô KÍNH FIX
	KÍCH THƯỚC	3000X6600 mm
VÁCH KÍNH	SỐ LƯỢNG	01

GHI CHÚ: TRƯỚC KHI GIA CÔNG CỬA CẦN KIỂM TRA KĨ KÍCH THƯỚC THỰC TẾ, NẾU CÓ SAI LỆCH CẦN BÁO NGAY CHO ĐƠN VỊ THIẾT KẾ ĐỂ KỊP THỜI XỬ LÝ

LẦN	NGÀY	NỘI DUNG SỬA ĐỔI

CHỦ ĐẦU TƯ - PROJECT OWNER:

ANH ĐỨC ANH

TÊN CÔNG TRÌNH - PROJECT:

BIỆT THỰ VƯỜN

HẠNG MỤC:

KIẾN TRÚC

VỊ TRÍ - LOCATION:

TỈNH HẢI PHÒNG

S - HOUSE DESIGN
INTERIOR DESIGN - CONSTRUCTION

CÔNG TY CỔ PHẦN
S-HOUSE VIỆT NAM
ĐỊA CHỈ: D49 LK7 Ô SỐ 1, KHU ĐÔ THỊ MỚI HAI BÊN ĐƯỜNG LÊ TRỌNG TẤN, PHƯỜNG DƯƠNG NỘI, THÀNH PHỐ HÀ NỘI.
TEL: 0966.005.060
WWW.NHADEPSHOUSE.COM

GIÁM ĐỐC:
DIRECTOR:

GĐ. NGUYỄN VĂN SANG

CHỦ TRÌ KIẾN TRÚC :
PRIMARY ARCHITECT:

KTS.TRƯƠNG QUANG NHẬT

CHỦ TRÌ KẾT CẤU
STRUCTURAL DESIGNER:

KS. ĐỖ MINH KHUÊ

THIẾT KẾ
DESIGNED BY:

KTS. NGUYỄN QUỐC BẢO


TÊN BẢN VẼ:
DRAWING NAME:


CHI TIẾT CỬA


TỶ LỆ - SCALE:	BẢN VẼ SỐ:
1/20	KT- 56
TÊN FILE - PATH FILE:	
.....	

GHI CHÚ/NOTE:


- Kích thước trên bản vẽ phải được kiểm tra thực tế tại công trình, nếu có sai lệch kích thước tại hiện trường phải báo thiết kế kịp thời để trao đổi phương án xử lý. Người thiết kế sẽ không chịu trách nhiệm kích thước tại công trình.
- Bản vẽ & thiết kế thuộc quyền sở hữu của Công ty CP S-House, không được sao chép nếu không có sự chấp thuận từ S-House.
- Hướng cửa xem trên mặt bằng định vị cửa

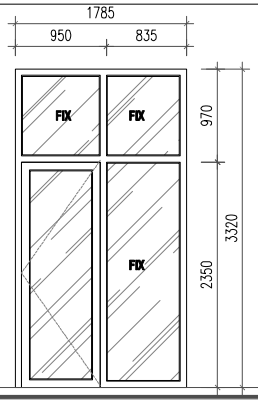

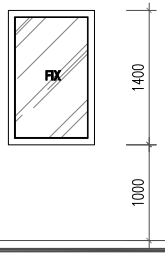

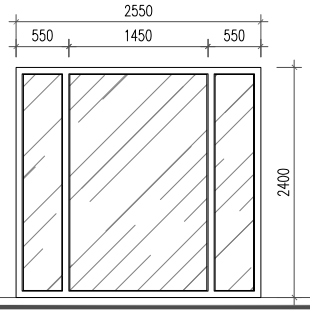


Bên trong

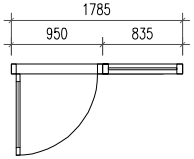

Bên ngoài

VK4	QUY CÁCH	CỬA ĐI KHUNG NHÔM KÍNH 1 CÁNH MỞ + Ô KÍNH FIX
	KÍCH THƯỚC	1785X3320 mm
VÁCH KÍNH	SỐ LƯỢNG	02


Bên trong

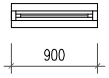

Bên ngoài


VK5	QUY CÁCH	KHUNG NHÔM + Ô KÍNH FIX
	KÍCH THƯỚC	900X1400 mm
VÁCH KÍNH	SỐ LƯỢNG	01

Bên trong

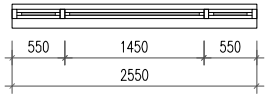


Bên ngoài

VK6	QUY CÁCH	KHUNG NHÔM + Ô KÍNH FIX
	KÍCH THƯỚC	2550X2400 mm
VÁCH KÍNH	SỐ LƯỢNG	01

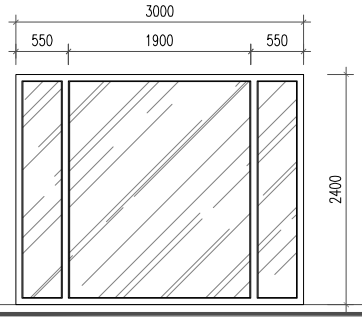

Bên trong

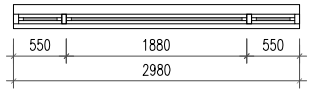

Bên ngoài

VK7	QUY CÁCH	KHUNG NHÔM + Ô KÍNH FIX
	KÍCH THƯỚC	2980X2400 mm
VÁCH KÍNH	SỐ LƯỢNG	01

GHI CHÚ: TRƯỚC KHI GIA CÔNG CỬA CẦN KIỂM TRA KĨ KÍCH THƯỚC THỰC TẾ, NẾU CÓ SAI LỆCH CẦN BÁO NGAY CHO ĐƠN VỊ THIẾT KẾ ĐỂ KỊP THỜI XỬ LÝ

LẦN	NGÀY	NỘI DUNG SỬA ĐỔI

CHỦ ĐẦU TƯ - PROJECT OWNER:

ANH ĐỨC ANH

TÊN CÔNG TRÌNH - PROJECT:

BIỆT THỰ VƯỜN

HẠNG MỤC:

KIẾN TRÚC

VỊ TRÍ - LOCATION:

TỈNH HẢI PHÒNG

S - HOUSE DESIGN
INTERIOR DESIGN - CONSTRUCTION

CÔNG TY CỔ PHẦN
S-HOUSE VIỆT NAM
ĐỊA CHỈ: D49 LK7 Ô SỐ 1, KHU ĐÔ THỊ MỚI HAI BÊN ĐƯỜNG LÊ TRỌNG TẤN, PHƯỜNG DƯƠNG NỘI, THÀNH PHỐ HÀ NỘI.
TEL: 0966.005.060
WWW.NHADEPSHOUSE.COM

GIÁM ĐỐC:
DIRECTOR:

GĐ. NGUYỄN VĂN SANG

CHỦ TRÌ KIẾN TRÚC :
PRIMARY ARCHITECT:

KTS.TRƯƠNG QUANG NHẬT

CHỦ TRÌ KẾT CẤU
STRUCTURAL DESIGNER:

KS. ĐỖ MINH KHUÊ

THIẾT KẾ
DESIGNED BY:

KTS. NGUYỄN QUỐC BẢO

TÊN BẢN VẼ:
DRAWING NAME:

CHI TIẾT CỬA

TỶ LỆ - SCALE:	BẢN VẼ SỐ:
1/20	KT- 57
TÊN FILE - PATH FILE:	

GHI CHÚ/NOTE:

- Kích thước trên bản vẽ phải được kiểm tra thực tế tại công trình, nếu có sai lệch kích thước tại hiện trường phải báo thiết kế kịp thời để trao đổi phương án xử lý. Người thiết kế sẽ không chịu trách nhiệm kích thước tại công trình.
- Bản vẽ & thiết kế thuộc quyền sở hữu của Công ty CP S-House, không được sao chép nếu không có sự chấp thuận từ S-House.
- Hướng cửa xem trên mặt bằng định vị cửa